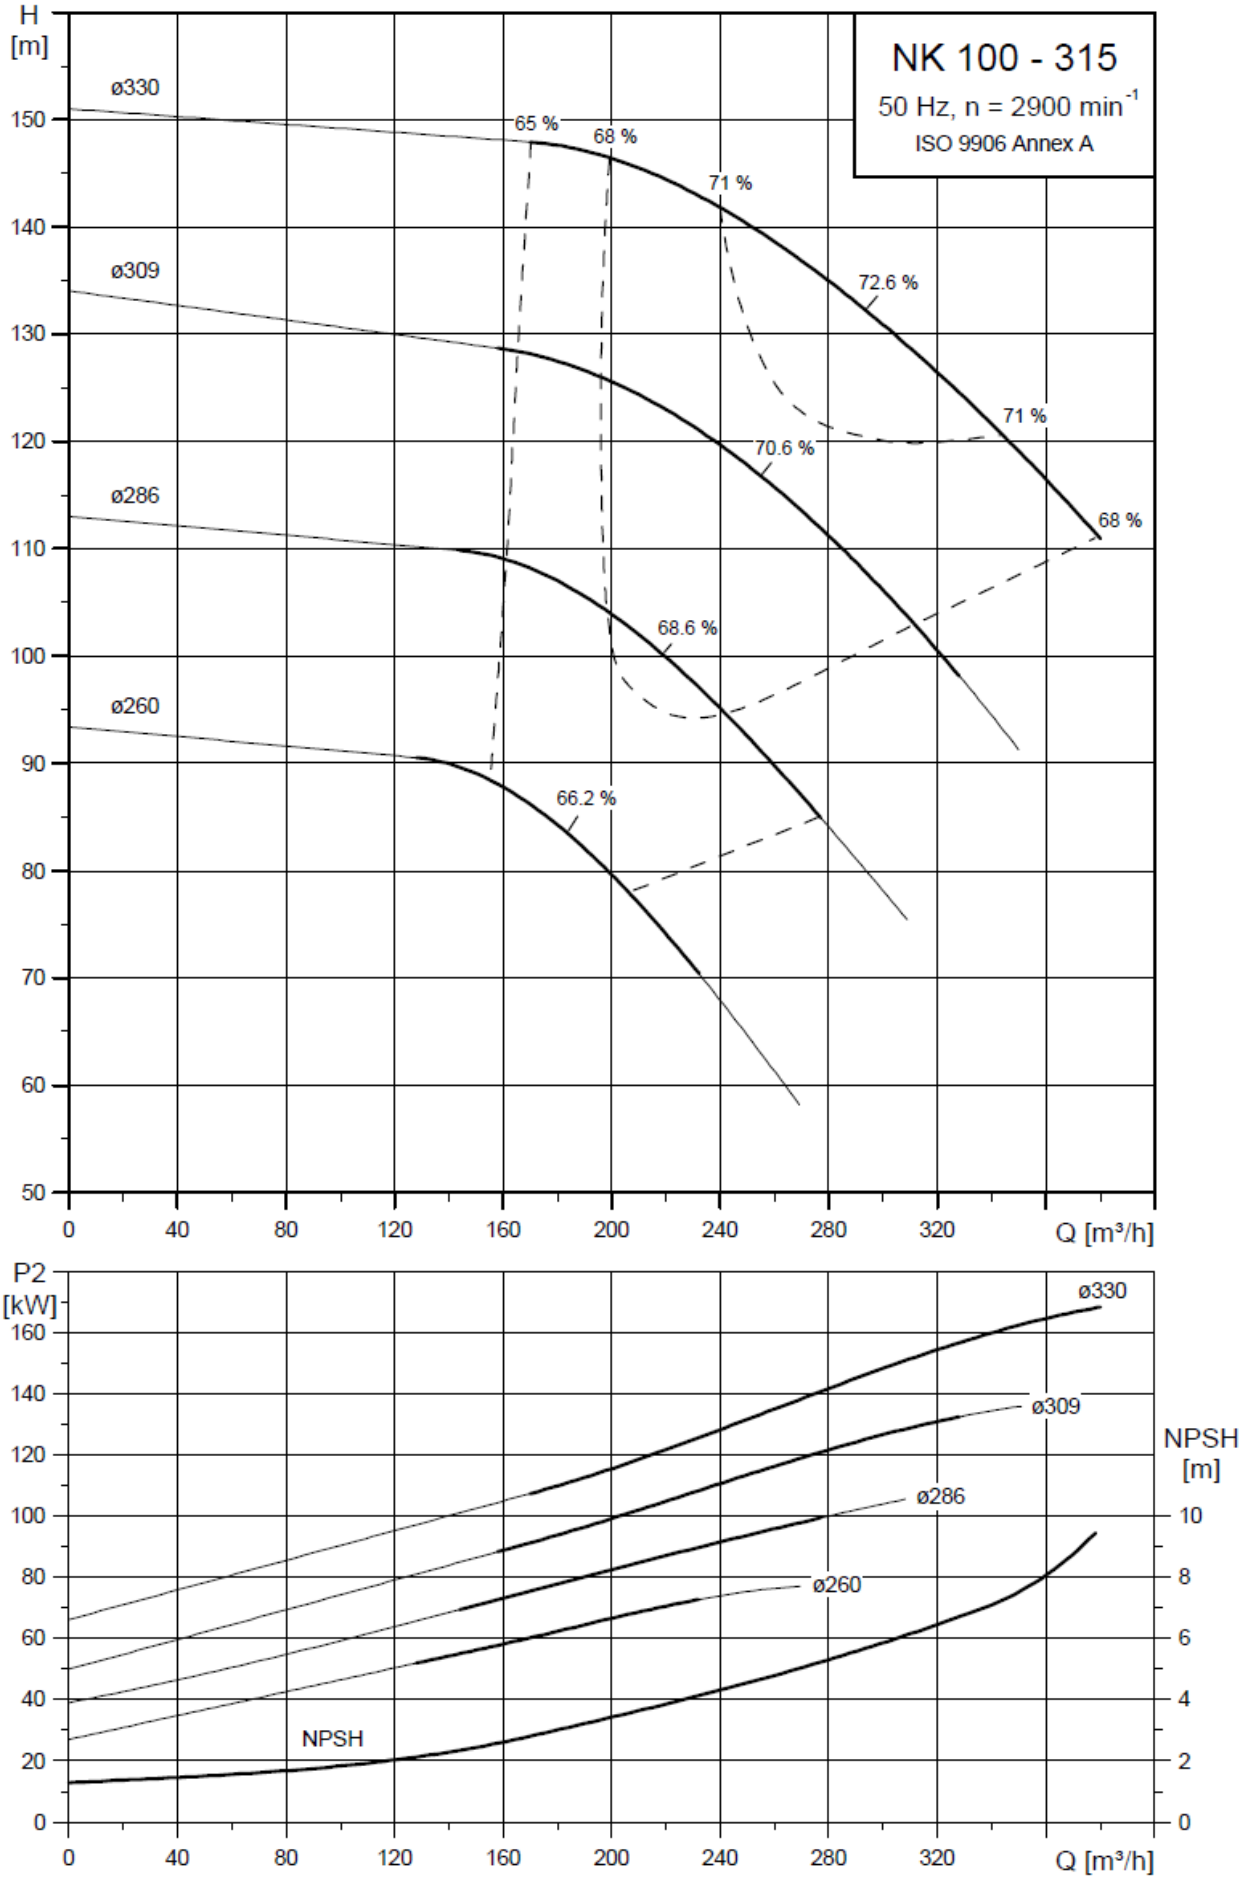

NK 100 - 315
50 Hz, n = 2900 min-1
ISO 9906 Annex A
H [m]
ø330
ø309
ø286
ø260
65 %
68 %
71 %
72.6 %
71 %
70.6 %
68 %
68.6 %
66.2 %
Q [m³/h]
P2 [kW]
NPSH
NPSH [m]